







PUNTO	NORTE	ESTE
1	1075879.959	857757.891
2	1075805.610	857777.880
3	1075793.829	857741.753
4	1075868.178	857721.763
5	1075864.148	857709.403
6	1075789.799	857729.393
7	1075778.639	857695.167
8	1075852.988	857675.177
9	1075848.003	857659.889
10	1075773.654	857679.879
11	1075761.873	857643.751
12	1075836.222	857623.761
13	1075832.812	857613.303
14	1075758.463	857633.293
15	1075747.613	857600.017
16	1075821.962	857580.027
17	1075817.002	857564.816
18	1075742.653	857584.805
19	1075730.872	857548.678
20	1075805.221	857528.688
21	1075801.811	857518.230
22	1075727.462	857538.220
23	1075716.612	857504.944
24	1075790.961	857484.954
25	1075786.001	857469.742
26	1075711.652	857489.732
27	1075685.611	857409.871
28	1075759.960	857389.881
29	1075754.999	857374.669
30	1075680.650	857394.659
31	1075668.870	857358.531
32	1075743.219	857338.196
33	1075739.809	857328.083
34	1075665.460	857348.073
35	1075654.610	857314.797
36	1075728.959	857294.808
37	1075723.998	857279.596
38	1075649.649	857299.586
39	1075637.869	857263.458
40	1075712.218	857243.468
41	1075708.808	857233.010
42	1075634.459	857253.000
43	1075623.608	857219.724
44	1075697.957	857199.734
45	1075692.997	857184.522
46	1075618.648	857204.512
47	1075606.868	857168.384
48	1075681.217	857148.394
49	1075677.187	857136.035
50	1075602.838	857156.025
51	1075595.397	857133.207
52	1075669.746	857113.218
53	1076119.279	857694.582
54	1076044.580	857713.854
55	1076032.852	857677.709
56	1076107.551	857658.437
57	1076103.538	857646.072
58	1076028.840	857665.344
59	1076017.728	857631.102
60	1076092.427	857611.829
61	1076087.489	857596.610
62	1076012.790	857615.883
63	1076001.062	857579.738
64	1076075.760	857560.466
65	1076072.365	857550.003
66	1075997.667	857569.275
67	1075986.864	857535.984
68	1076061.563	857516.711
69	1076056.624	857501.493
70	1075981.926	857520.765
71	1075970.197	857484.620
72	1076044.896	857465.348
73	1076041.501	857454.885
74	1075966.802	857474.157
75	1075956.000	857440.866
76	1076030.698	857421.594
77	1076025.760	857406.375
78	1075951.061	857425.647
79	1075939.333	857389.502
80	1076014.032	857370.230

PUNTO	NORTE	ESTE
81	1076010.636	857359.767
82	1075935.938	857379.039
83	1075925.135	857345.748
84	1075999.834	857326.476
85	1075994.896	857311.257
86	1075920.197	857330.529
87	1075908.469	857294.385
88	1075983.167	857275.112
89	1075979.772	857264.649
90	1075905.073	857283.922
91	1075894.271	857250.630
92	1075968.970	857231.358
93	1075964.031	857216.139
94	1075889.333	857235.412
95	1075877.604	857199.267
96	1075952.303	857179.994
97	1075948.908	857169.532
98	1075917.922	857177.526
99	1075888.857	857087.953
100	1075922.494	857088.130
101	1075905.253	857180.795
102	1075874.267	857188.789
103	1075841.886	857088.997
104	1075875.242	857088.308
105	1076140.928	857429.201
106	1076058.468	857450.476
107	1076047.666	857417.184
108	1076130.125	857395.910
109	1076125.187	857380.691
110	1076042.727	857401.966
111	1076030.999	857365.821
112	1076113.458	857344.546
113	1076110.063	857334.083
114	1076027.604	857355.358
115	1076016.801	857322.067
116	1076099.261	857300.792
117	1076094.322	857285.573
118	1076011.863	857306.848
119	1076000.134	857270.703
120	1076082.594	857249.428
121	1076079.199	857238.965
122	1075996.739	857260.240
123	1075985.937	857226.949
124	1076068.396	857205.674
125	1076063.458	857190.455
126	1075980.999	857211.730
127	1075969.270	857175.585
128	1076051.730	857154.310
129	1075992.504	857158.283
130	1075961.519	857166.278
131	1075936.519	857089.232
132	1075970.282	857089.799
133	1075980.326	857094.881
134	1076000.251	857156.285
135	1076020.391	857151.089
136	1076003.482	857098.977
137	1076010.187	857098.582
138	1076026.678	857149.403
139	1076051.377	857143.094
140	1076035.921	857095.463
141	1076044.708	857094.386
142	1076139.785	857082.837
143	1076150.998	857117.392
144	1076059.807	857140.919
145	1076067.558	857150.227
146	1076150.018	857128.952
147	1076161.746	857165.097
148	1076079.287	857186.371
149	1076084.225	857201.590
150	1076166.685	857180.315
151	1076177.487	857213.607
152	1076095.028	857234.881
153	1076098.423	857245.344
154	1076180.882	857224.070
155	1076192.611	857260.214
156	1076110.151	857281.489
157	1076115.089	857296.708
158	1076197.549	857275.433
159	1076208.352	857308.724
160	1076125.892	857329.999

PUNTO	NORTE	ESTE
161	1076129.287	857340.462
162	1076211.747	857319.187
163	1076223.475	857355.332
164	1076141.016	857376.607
165	1076145.954	857391.826
166	1076228.413	857370.551
167	1076239.216	857403.842
168	1076156.756	857425.117
169	1076195.318	857426.539
170	1076242.620	857414.334
171	1076254.349	857450.479
172	1076206.817	857462.743
173	1076211.636	857477.910
174	1076259.263	857465.623
175	1076270.065	857498.914
176	1076222.501	857511.185
177	1076225.916	857521.643
178	1076273.460	857509.377
179	1076285.189	857545.522
180	1076237.665	857557.783
181	1076242.670	857572.984
182	1076290.127	857560.740
183	1076301.209	857594.990
184	1076253.932	857607.188
185	1076257.998	857619.539
186	1076305.251	857607.348
187	1076314.463	857641.904
188	1076269.446	857654.308
189	1076330.946	857633.525
190	1078564.085	857602.310
191	1078602.478	857592.394
191A	1078605.794	857595.126
192	1076402.361	857590.528
193	1076374.104	857576.183
194	1076317.111	857590.888
195	1076306.000	857556.645
196	1076397.977	857532.915
197	1076389.713	857518.554
198	1076301.061	857541.426
199	1076289.333	857505.282
200	1076370.123	857484.438
201	1076364.488	857474.552
202	1076285.938	857494.819
203	1076281.378	857480.767
204	1076355.718	857459.169

PUNTO	NORTE	ESTE
1	1075928.493	857087.293
6	1075829.749	857089.046
32	1076034.967	857721.488
36	1076132.390	857696.352
35	1076056.020	857462.191
34	1076198.219	857435.672
29	1076270.916	857658.774
28	1076405.062	857545.218
27	1076355.718	857459.169
26	1076258.783	857425.265
14	1076150.068	857081.883

PUNTO	NORTE	ESTE
37	1075680.643	857108.741
48	1075892.630	857759.654
49	1075796.049	857786.092
65	1075581.463	857127.568

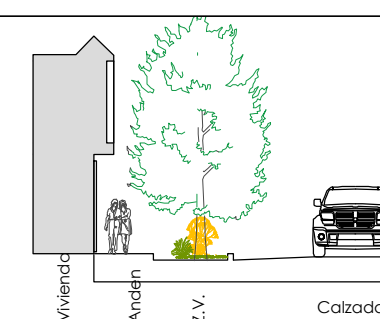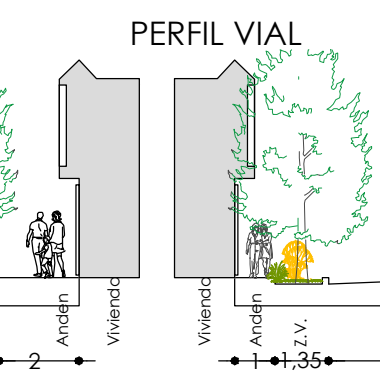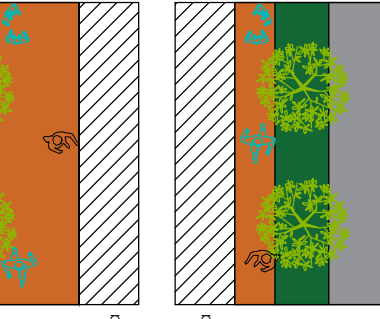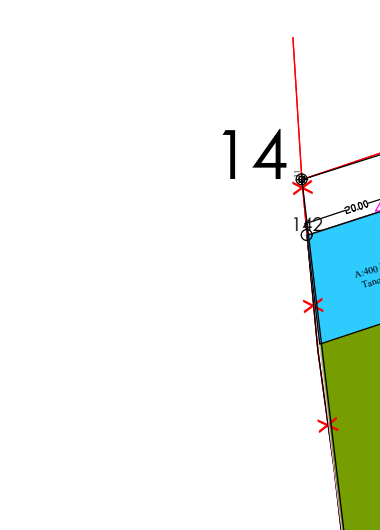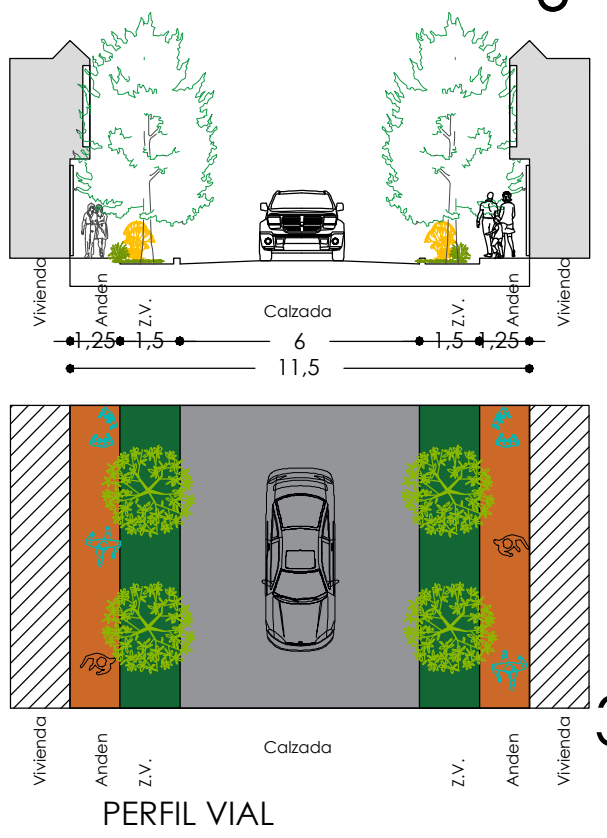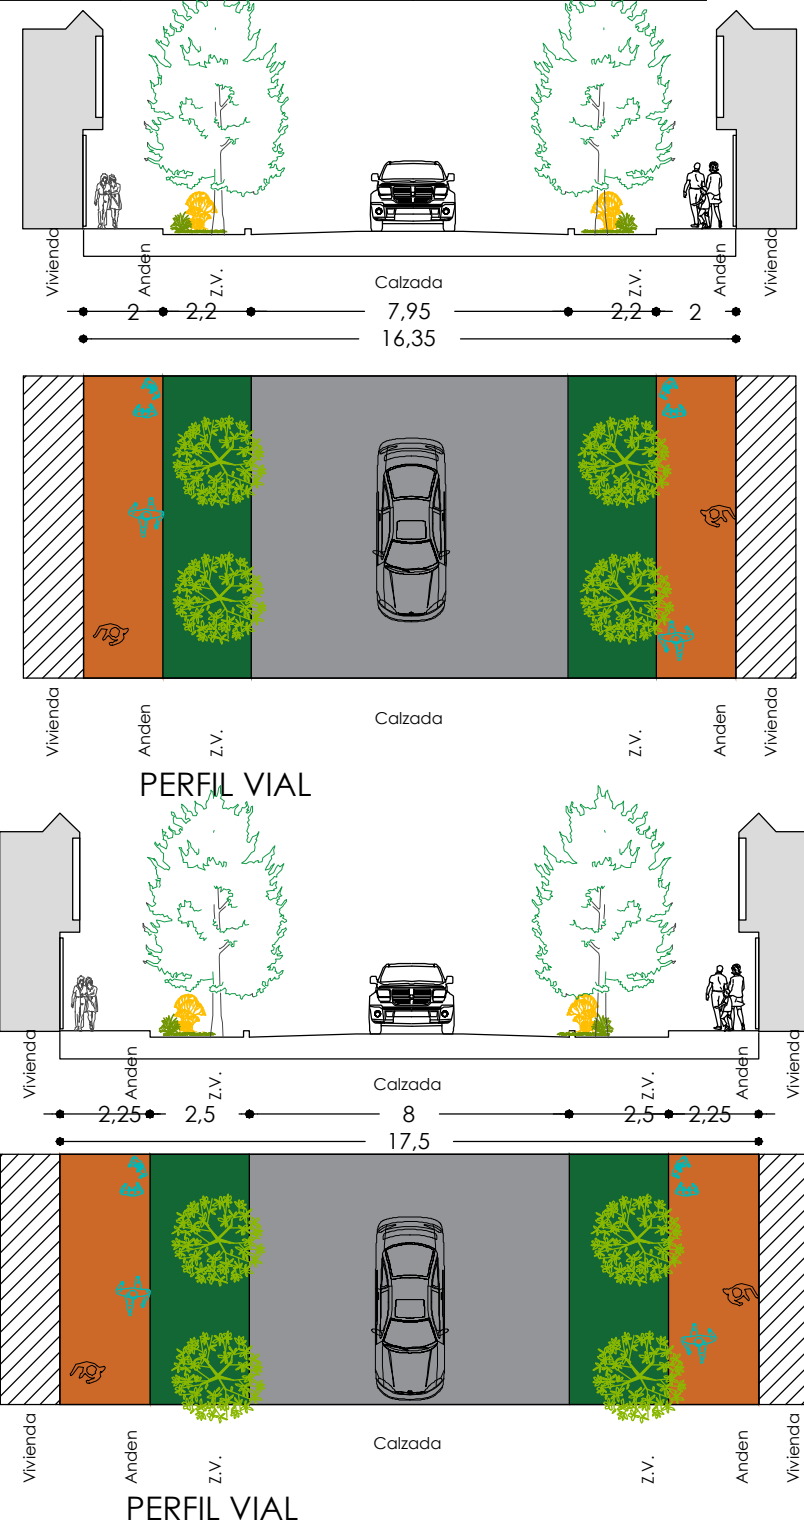

NUEVA GRANADA

LUIS GALAN
PTO 37 - PTO 65
L=101.32 m

FISCAL
PTO 32 - PTO 6
L=664.91 m

FISCAL
PTO 37 - PTO 48
L=684.80 m

EDGAR VILLANUEVA
PTO 65 - PTO 49
L=692.17 m

CUADRO DE AREAS

CUADRO DE AREAS ESCRITURAS			%
ETAPA I	67950 M2	100	
ETAPA II	65234 M2		
ETAPA III	76131.85 M2		
ETAPA IV	26299 M2		
NUEVA GRANADA	235614.85 M2		
CUADRO DE AREAS NUEVA GRANADA			%
AREA URBANIZABLE	138863.21 M2	58.94	
EQUIPAMIENTO	1739.237 M2	0.74	
ZONA VERDE	8053.13 M2	3.42	
VIAS	86959.273 M2	36.91	
AREA TOTAL LOTE	235614.85 M2	100	

